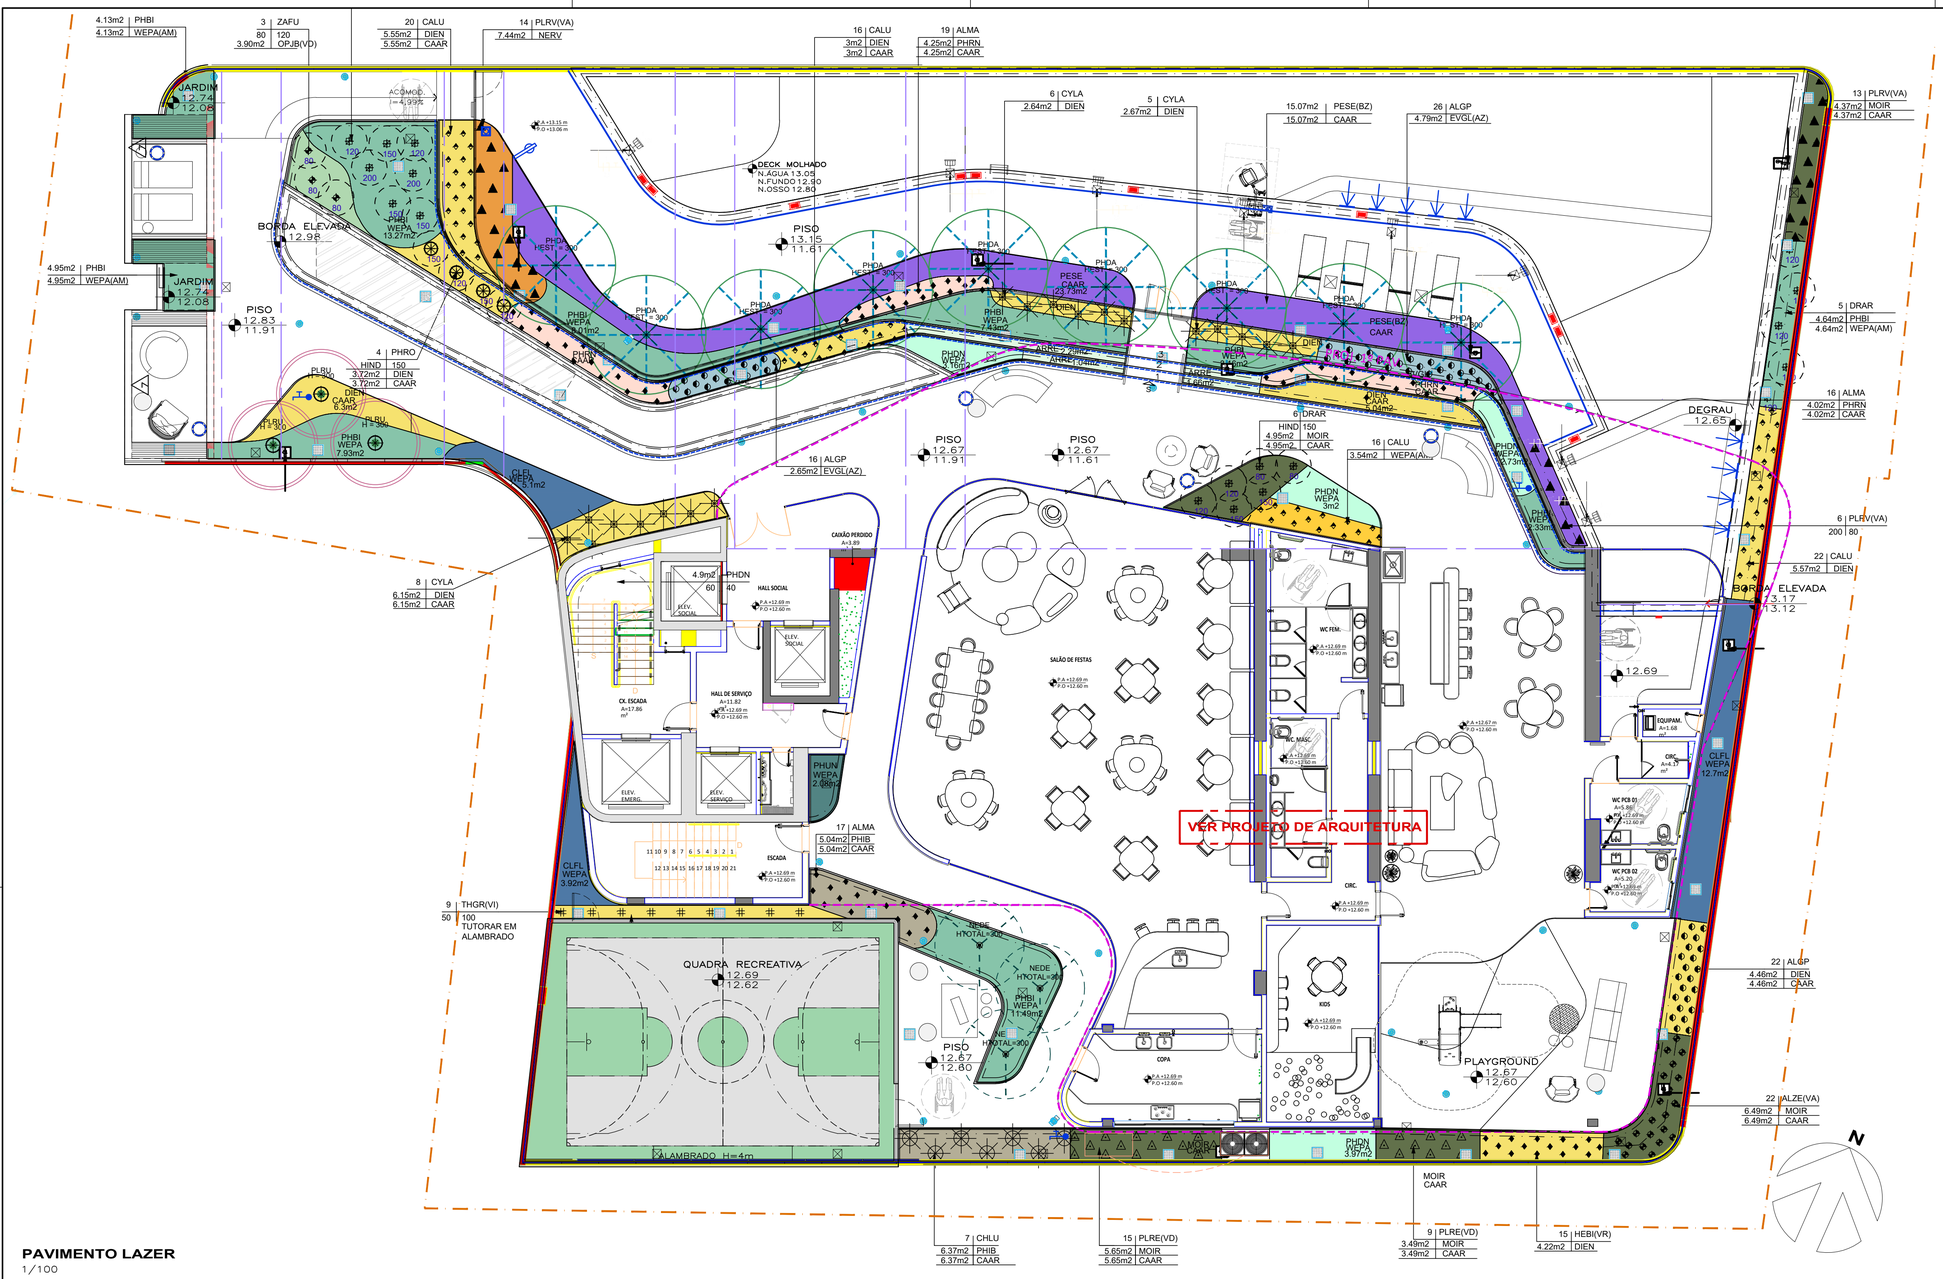

PAVIMENTO LAZER
1/100

LEGENDA GERAL

QUANTIDADE | CÓDIGO (COR/PODA)
PORTE (cm) | DIST.PLANTIO (cm)

LINHA DIVISÓRIA DE FORRAÇÕES
LINHA DIVISÓRIA DE ORLAS
ÁRVORE EXISTENTE
PALMEIRA EXISTENTE
CACHEPÔ
VASO
SEIXOS/PEDRISCOS
ÁRVORES QUOTA AMBIENTAL
ÁRVORES COMPENSAÇÃO

LEGENDA DE CORES DAS ESPÉCIES VEGETAIS

AM = amarelo	LI = lilás	SU = sulferina
AZ = azul	MU = multicolor	TI = tijolo
BR = branco	PU = púrpura	VA = variegata
BZ = bronze	RS = rosa	VI = violeta
CH = champagne	RX = roxo	VD = verde
LA = laranja	SA = salmon	VR = vermelho

O PROJETO DE PLANTIO QUE ESTÁ EM OUTRA(S) FOLHA(S) NÃO PODERÁ SER EXECUTADO OU ORÇADO SEM QUE AS INFORMAÇÕES DESTA SEJAM SEGUIDAS

OS DETALHES GERAIS E NOTAS IMPORTANTES ESTÃO EM UM FOLHA A PARTE E DEVEM SER SEGUIDAS PARA ORÇAMENTO E EXECUÇÃO DO PLANTIO

A PLOTAGEM DESTA FOLHA DEVERÁ SER COLORIDA

ARRE | CLFL WEPA | DIEN CAAR | EVGL | NERV | OPJB (VD)
PESE(BZ) CAAR | PHBI WEPA | PHDN WEPA | PHIB CAAR | PHRN CAAR | THWI WEPA

TABELA DE ESPÉCIES VEGETAIS PAVIMENTO LAZER

CÓDIGO	NOME CIENTÍFICO	NOME POPULAR	QTDE. unid.	PORTE cm	DIST. PLANTIO cm	ESPECIFICAÇÕES	COR	CAULE Øcm	PODA
ALGP	Alpinia giant pink shell	Alpinia rosa gigante	64	200	40	Muda bem formada			
ALMA	Alocasia macrorrhizos	Alocasia	70	100	60	Muda bem formada			
ALZE	Alpinia zerumbet variegata	Alpinia variegata	22	100	50	Muda bem formada	VA		
CALU	Calathea lutea	Calatéia charuto	74	150	50	Muda bem formada – ver det			
CHLU	Chrysalidocarpus lutescens lu	Areca s/ folhas embaixo	7	250	100	Muda com 5 hastes podada embaixo			
CYLA	Cyrtostachys lakka	Laka	19	200	100	Muda bem formada – ver det			
DRAR	Dracaena arborea	Dracena arbórea	7	200	150	Muda bem formada			
DRAR	Dracaena arborea	Dracena arbórea	2	80	150	Muda bem formada			
DRAR	Dracaena arborea	Dracena arbórea	4	120	150	Muda bem formada			
DRAR	Dracaena arborea	Dracena arbórea	5	150	150	Muda bem formada			
HEBI	Heliconia bihai	Heliconia alta	15	200	50	Muda bem formada	VR		
NEDE	Neodypsis decaryi	Neodypsis	3	HTOTAL=300	300	Tutorar muda bem formada – ver det			
PHDA	Phoenix dactylifera	Tamareira	9	HESTIPE=300	400	Tutorar muda bem formada–ver det			
PHRO	Phoenix roebelinii	Tamareira anã	2	HESTIPE=120	150	Muda bem formada – ver det			
PHRO	Phoenix roebelinii	Tamareira anã	2	HESTIPE=150	150	Muda bem formada – ver det			
PLRE	Pleomele reflexa	Pleomele	24	200	60	Muda bem formada	VD		
PLRU	Plumeria rubra	Plumeria	3	300	300	Tutorar muda bem formada–ver det	RS		
PLRV	Pleomele reflexa variegata	Pleomele variegata	33	200	80	Muda bem formada	VA		
THGR	Thunbergia grandiflora	Tumbergia	9	50	100	Muda enraizada–Tutorar c/ cabo de aço	VI		
ZAFU	Zamia furfuracea	Zamia	3	80	60	Muda bem formada			

TABELA DE FORRAÇÕES – PAVIMENTO LAZER

CÓDIGO	NOME CIENTÍFICO	NOME POPULAR	QTDE. m2	PORTE cm	DIST. PLANTIO cm	ESPECIFICAÇÕES	COR
ARRE	Arachis repens	Grama amendoim	5	10	10	Muda enraizada / 100mudas p/ m2	AM
CLFL	Clusia fluminensis	Clusia	22	80	40	Muda bem formada / 4mudas p/m2	
DIEN	Dianela ensifolia	Dianela	54	30	30	Muda enraizada/ 12muda p/ m2	
EVGL	Evolvulus glomeratus	Azulzinha	7.5	20	15	Muda enraizada / 45mudas p/ m2	AZ
MOIR	Moraea iridioides	Morea alto branco	25.5	30	15	Touceira enraizada em pote de 8litros / 45mudas p/ m2	BR
NERV	Nephrolepis rivularis	Samambaia	7.5	40	20	Muda enraizada / 25 mudas p/m2	
OPJB	Ophiopogon jaburan	Barba de serpente	4	20	15	Touceira enraizada / 45mudas p/ m2	VD
PESE	Pennisetum setaceum	capim–do–texas	39	40	40	Touceira enraizada / 6mudas p/ m2	BZ
PHBI	Philodendron bipinnatifidum	Guaimbê	65.5	40	35	Muda enraizada/ 8muda p/ m2	
PHDN	Philodendron danteanum	Filodendro danteanum	10.5	60	40	Muda enraizada / 6 mudas p/m2	
PHIB	Philodendron imbe	Filodendro Imbe	11.5	40	20	Muda enraizada / 25 mudas p/m2	
PHRN	Philodendron renauxii	Filodendro renauxi	11.5	60	25	Muda bem formada / 6 mudas p/m2	
PHUN	Philodendron undulatum	Filodendro	2.5	60	50	Muda bem formada / 5mudas p/ m2	VD
WEPA	Wedelia paludaris	Dorinha	125.5	15	20	Muda enraizada / 25mudas p/ m2	AM

CÁLCULO DE TERRA

PARA O CÁLCULO DA TERRA , NA EXECUÇÃO DO JARDIM, NÃO SOMAR AS FORRAÇÕES DESTA TABELA, POIS AS FORRAÇÕES PODEM ESTAR SOBREPOSTAS, GERANDO QUANTIDADES DUPLICADAS.

TABELA DE MATERIAIS (ORÇAR À PARTE) – PAVIMENTO TÉRREO

CÓDIGO	PRODUTO	QTDE. m3	QTDE. M/L	ALTURA DA CAMADA	COR
CAAR	Casca de árvore – de 6 a 8cm	6	--	5CM	--

REVISÃO	DATA	DESCRIÇÃO DAS REVISÕES	RESPONSÁVEL
00	01.04.25	EMISSÃO INICIAL	CAMILA M.

PAISAGISMO PININFARINA
AV.BEIRA MAR – FORTALEZA – CE

CLIENTE
DIAGONAL
CÓDIGO PROJETO
4080–013

TITULO
PLANTA PAVIMENTO LAZER

FASE
PROJETO DE PLANTIO

DIRETOR DE CRIAÇÃO: DAISY HUANG
COORDENADOR: CAMILA NICOLIELO
ARQ. PAISAGISTA: SAMIRA SAKAYANAGUI
CHECK–LIST:
LIBERADO:

FOLHA
PE.504
REVISÃO
00
ESCALA
1:100
EMISSÃO INICIAL
01.04.25
NOME ARQUIVO
PINI–PSG–PE–0504–LAZ–R00

BENEDITO ABBUD arquitetura paisagística
R. ARMINDA Nº93, 11ºANDAR, VILA OLIMPIA – SP FONE/FAX (011) 5056 9977 SITE: WWW.BENEDITOABBUD.COM.BR

NÃO ALTERAR ESTE PROJETO SEM PREVIA AUTORIZAÇÃO DO ARQUITETO PAISAGISTA