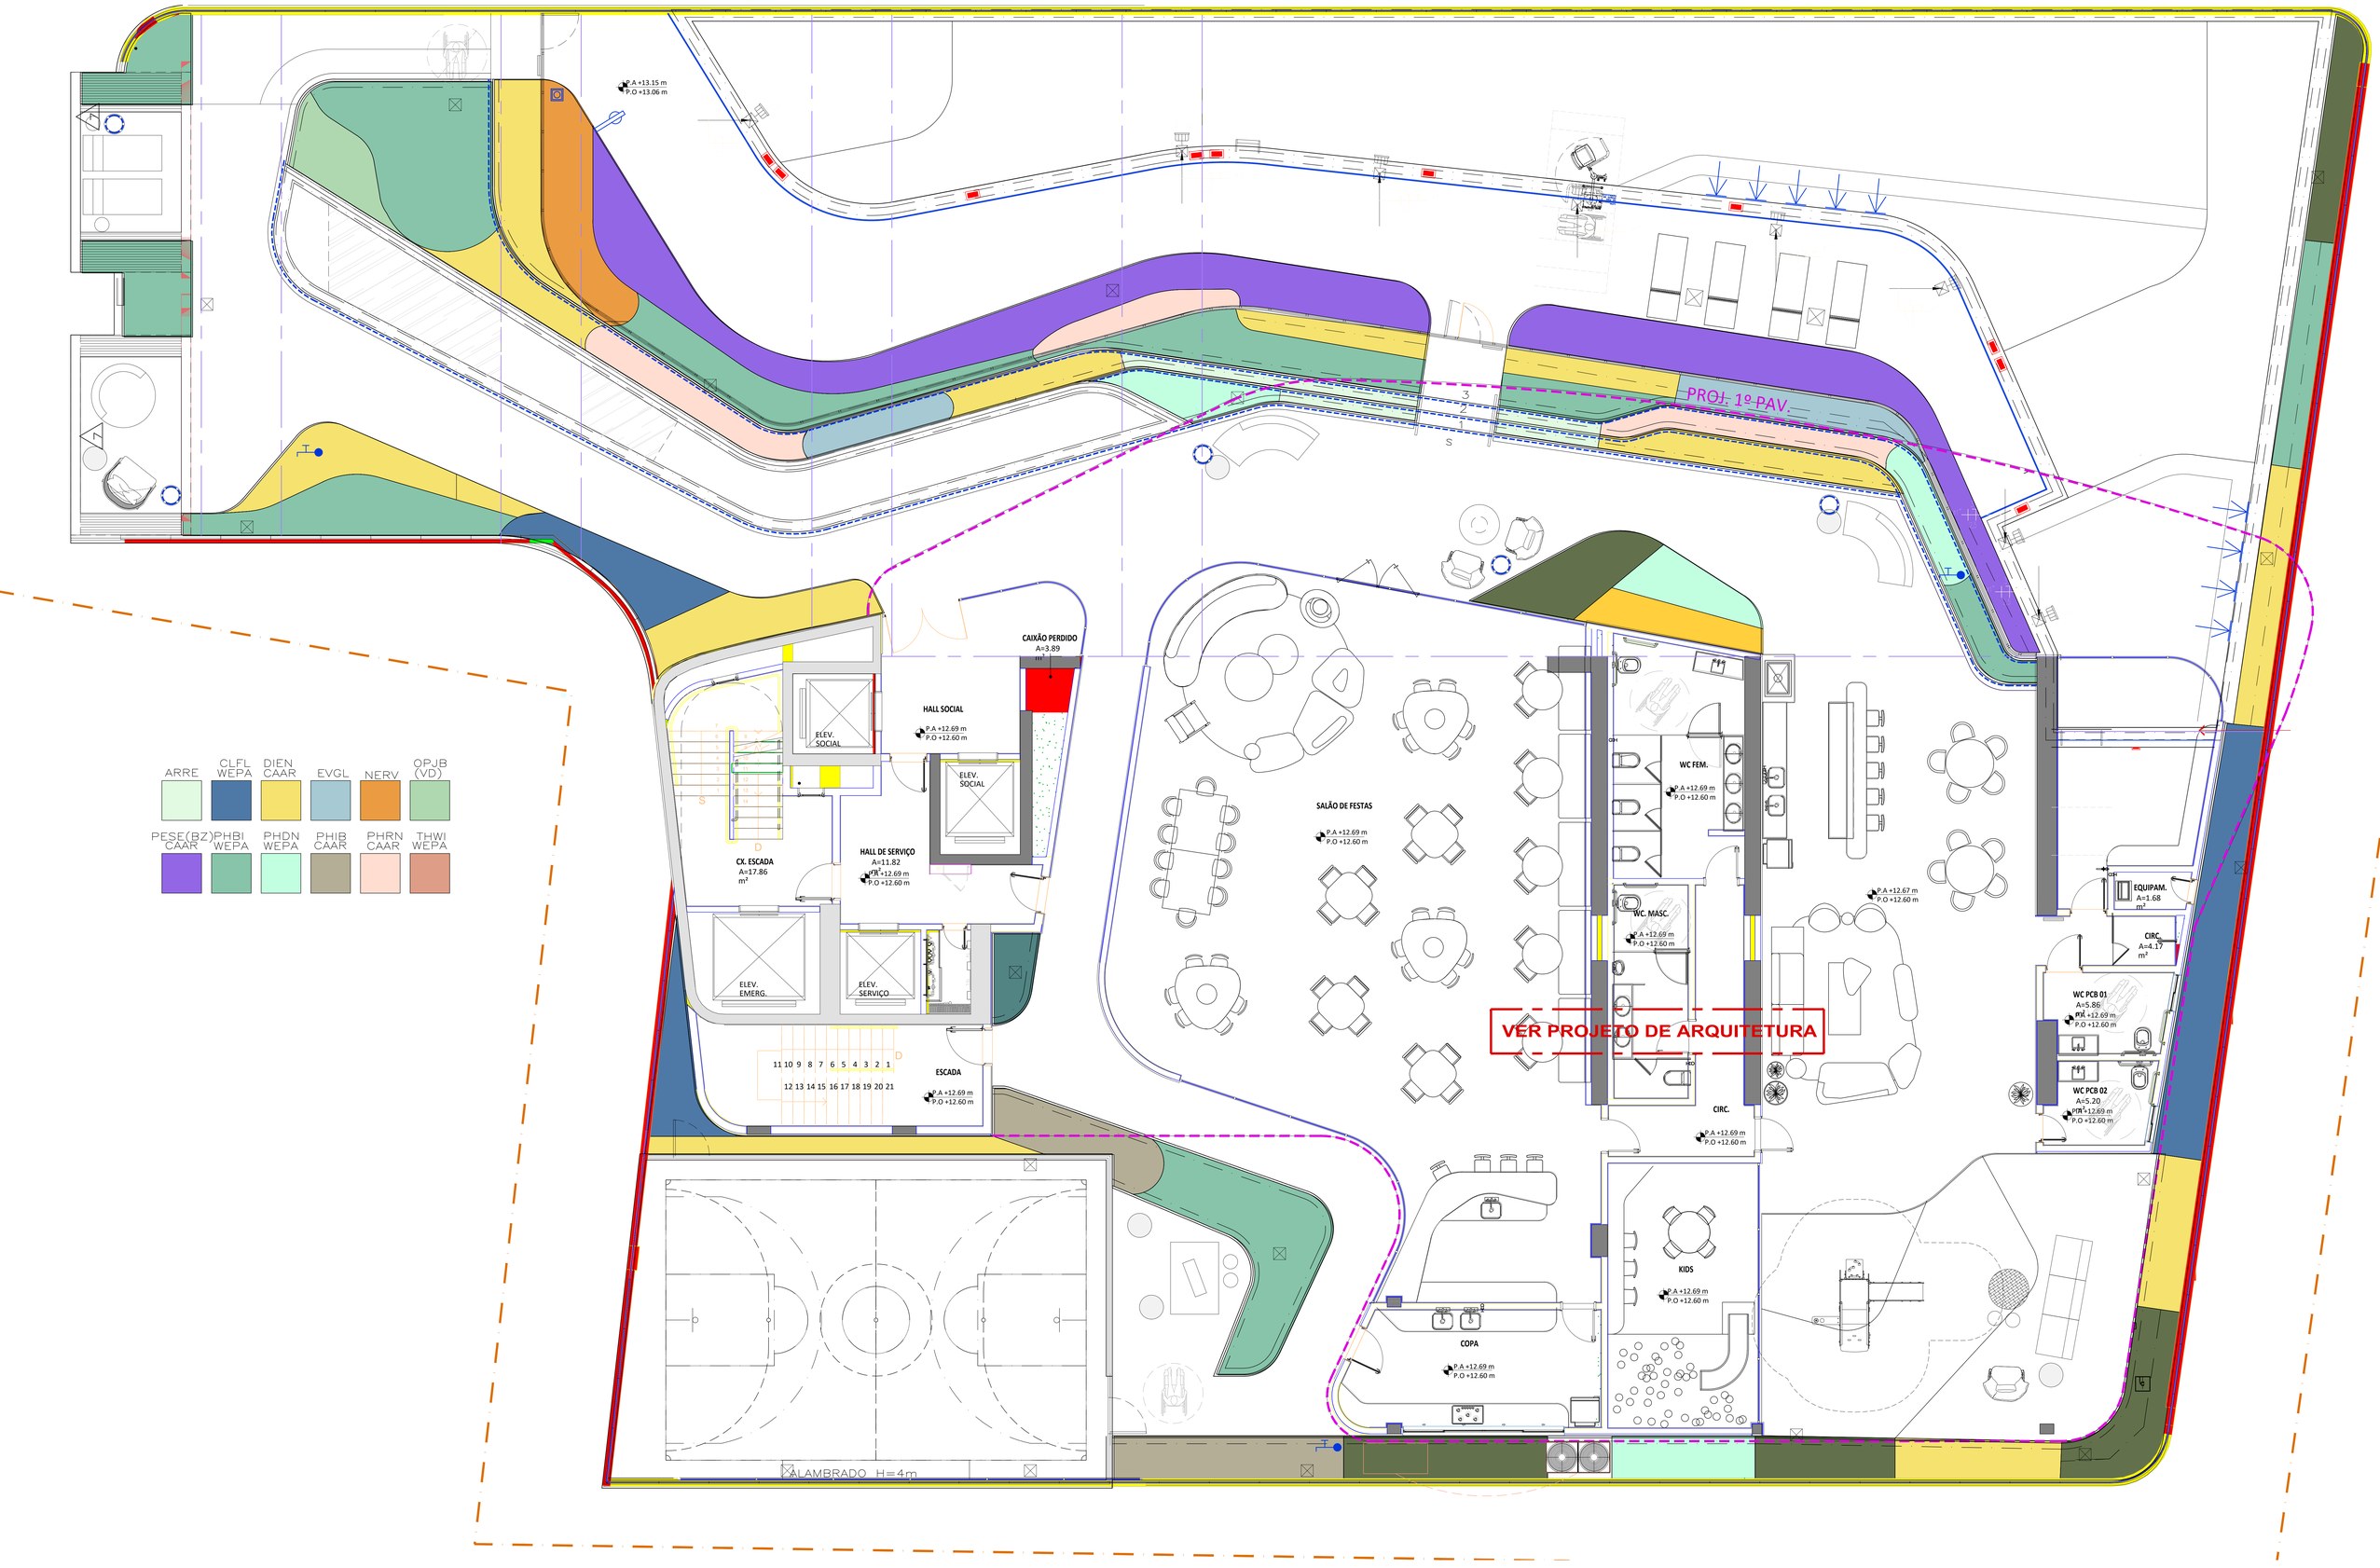
ARRE
CLFL WEPA
DIEN CAAR
EVGL
NERV
OPJB (VD)
PESE(BZ) CAAR
PHBI WEPA
PHDN WEPA
PHIB CAAR
PHRN CAAR
THWI WEPA
PROJ. 1º PAV.
P.A +13.15 m
P.O +13.06 m
CAIXÃO PERDIDO
A=3.89 m²
HALL SOCIAL
P.A +12.69 m
P.O +12.60 m
ELEV. SOCIAL
CX. ESCADA
A=17.86 m²
HALL DE SERVIÇO
A=11.82 m²
ELEV. EMERG.
ELEV. SERVIÇO
ESCADA
11 10 9 8 7 6 5 4 3 2 1
12 13 14 15 16 17 18 19 20 21
SALÃO DE FESTAS
WC FEM.
WC. MASC.
CIRC.
VER PROJETO DE ARQUITETURA
EQUIPAM.
A=1.68 m²
CIRC.
A=4.17 m²
WC PCB 01
A=5.86 m²
WC PCB 02
A=5.20 m²
KIDS
COPA
ALAMBRADO H=4m